




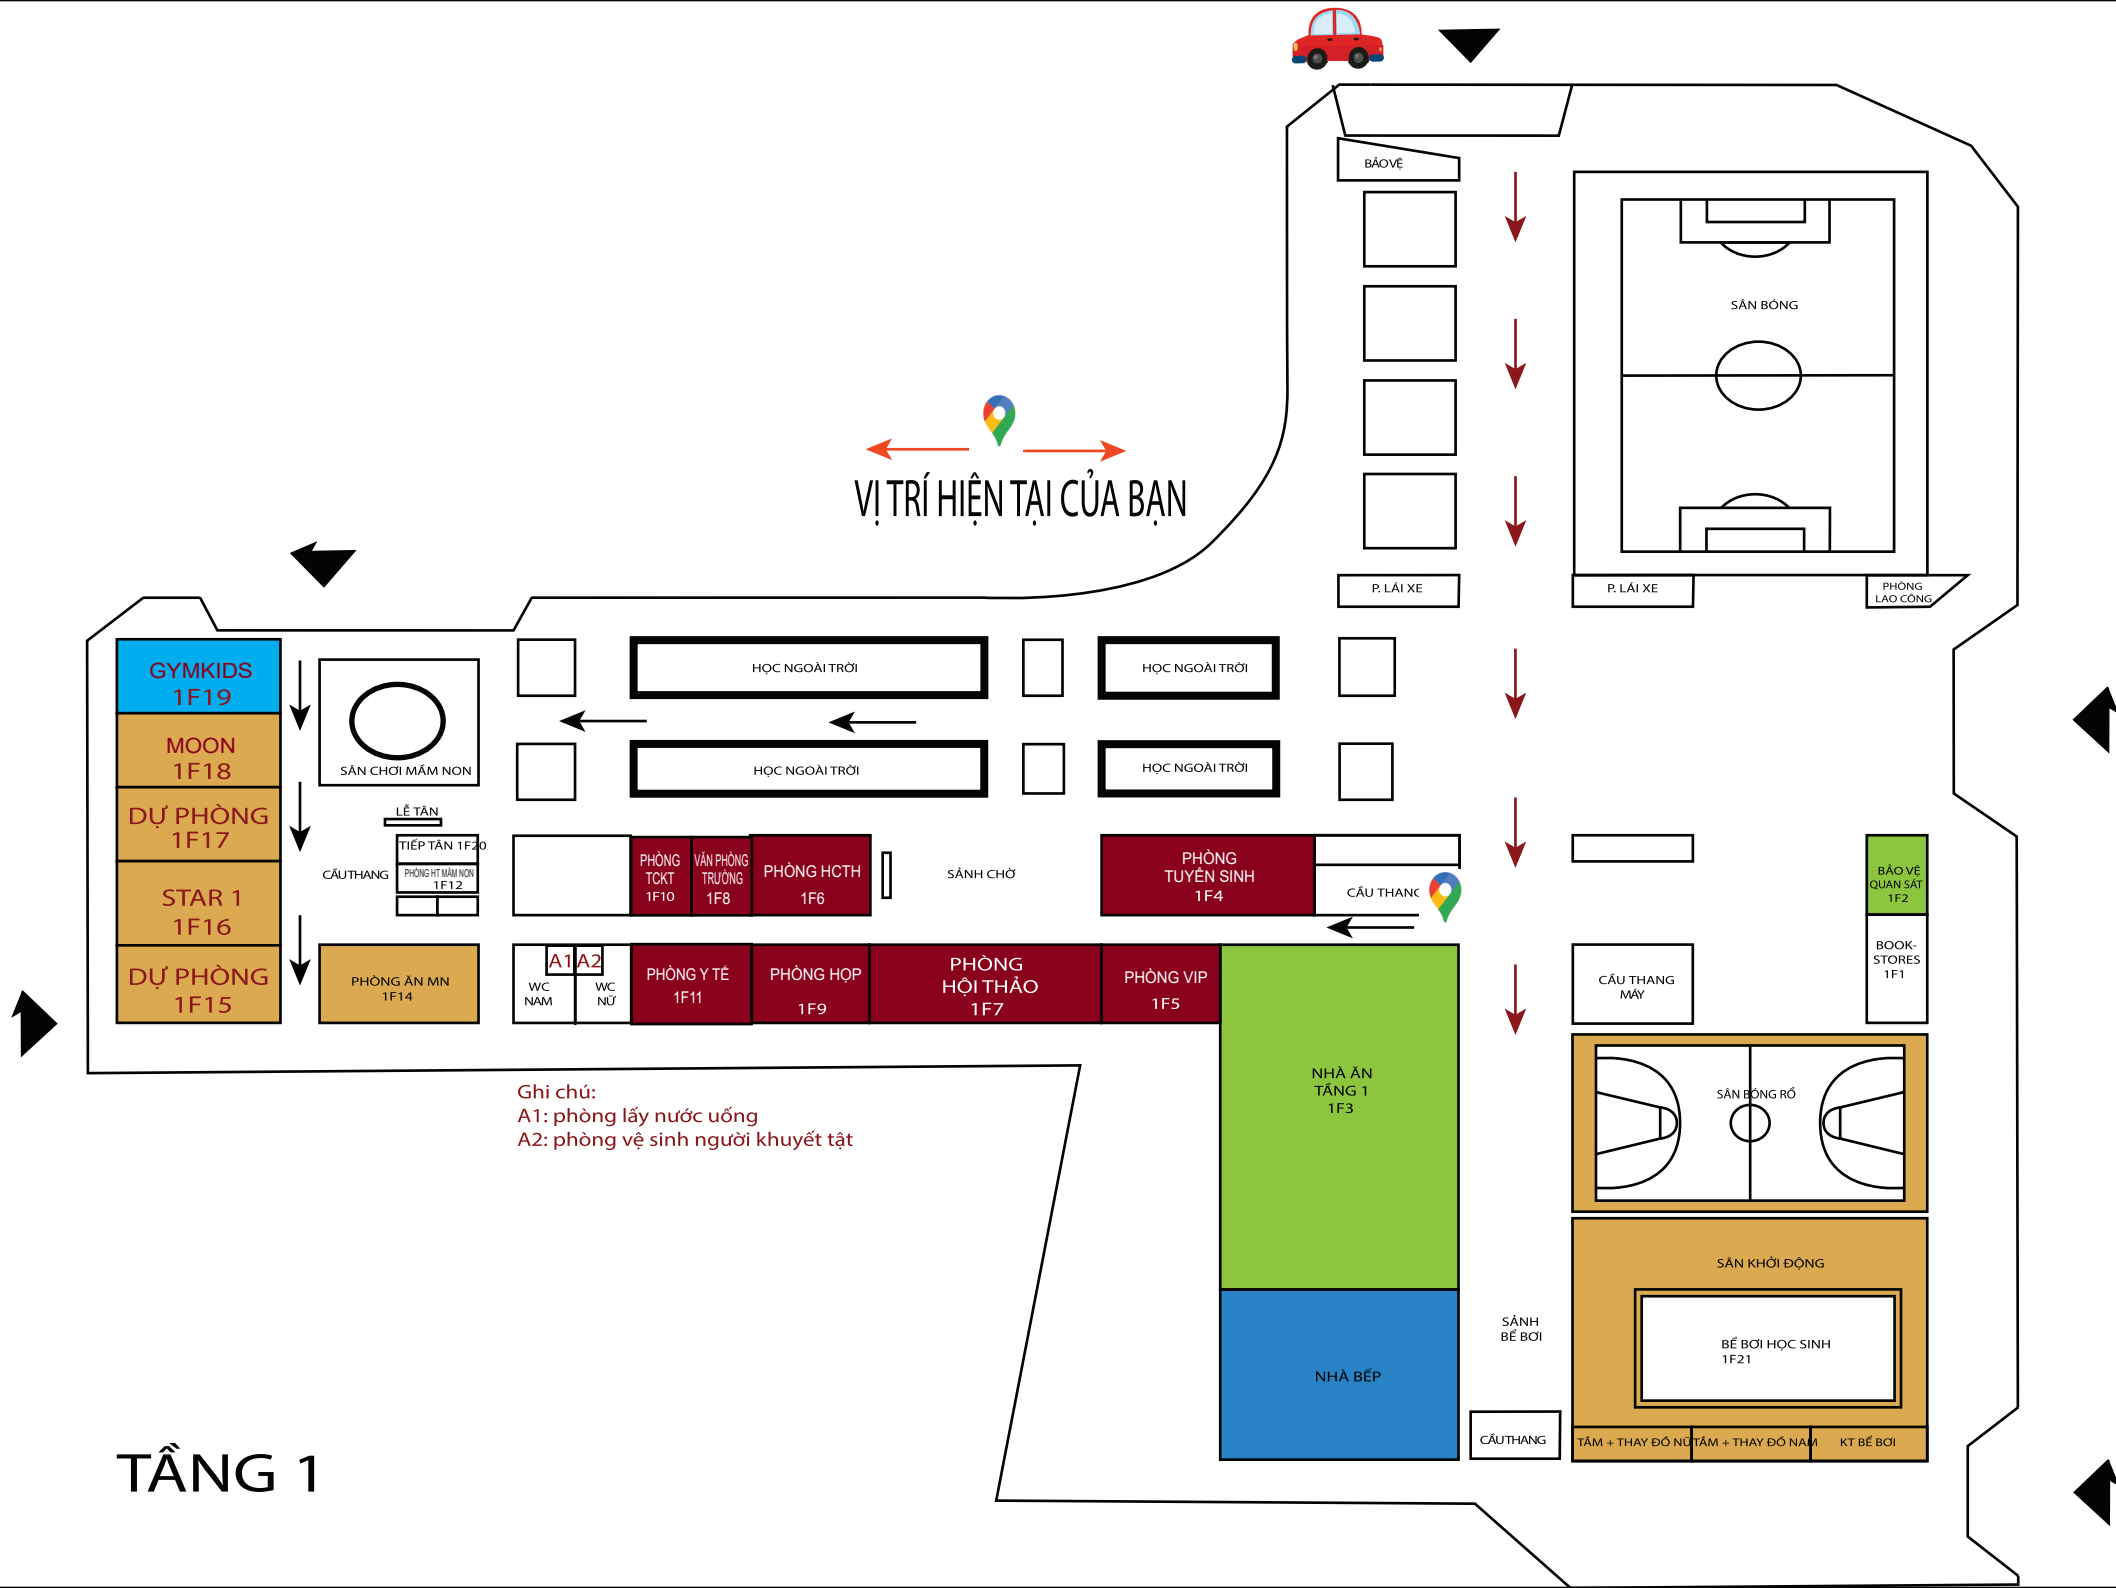

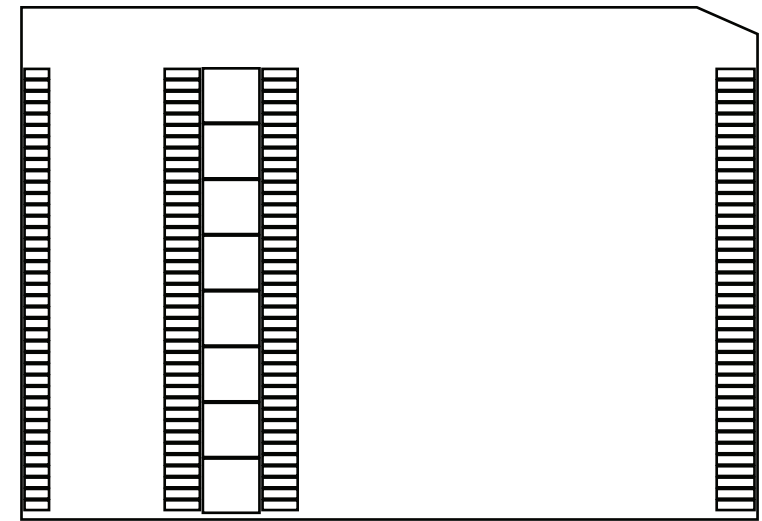


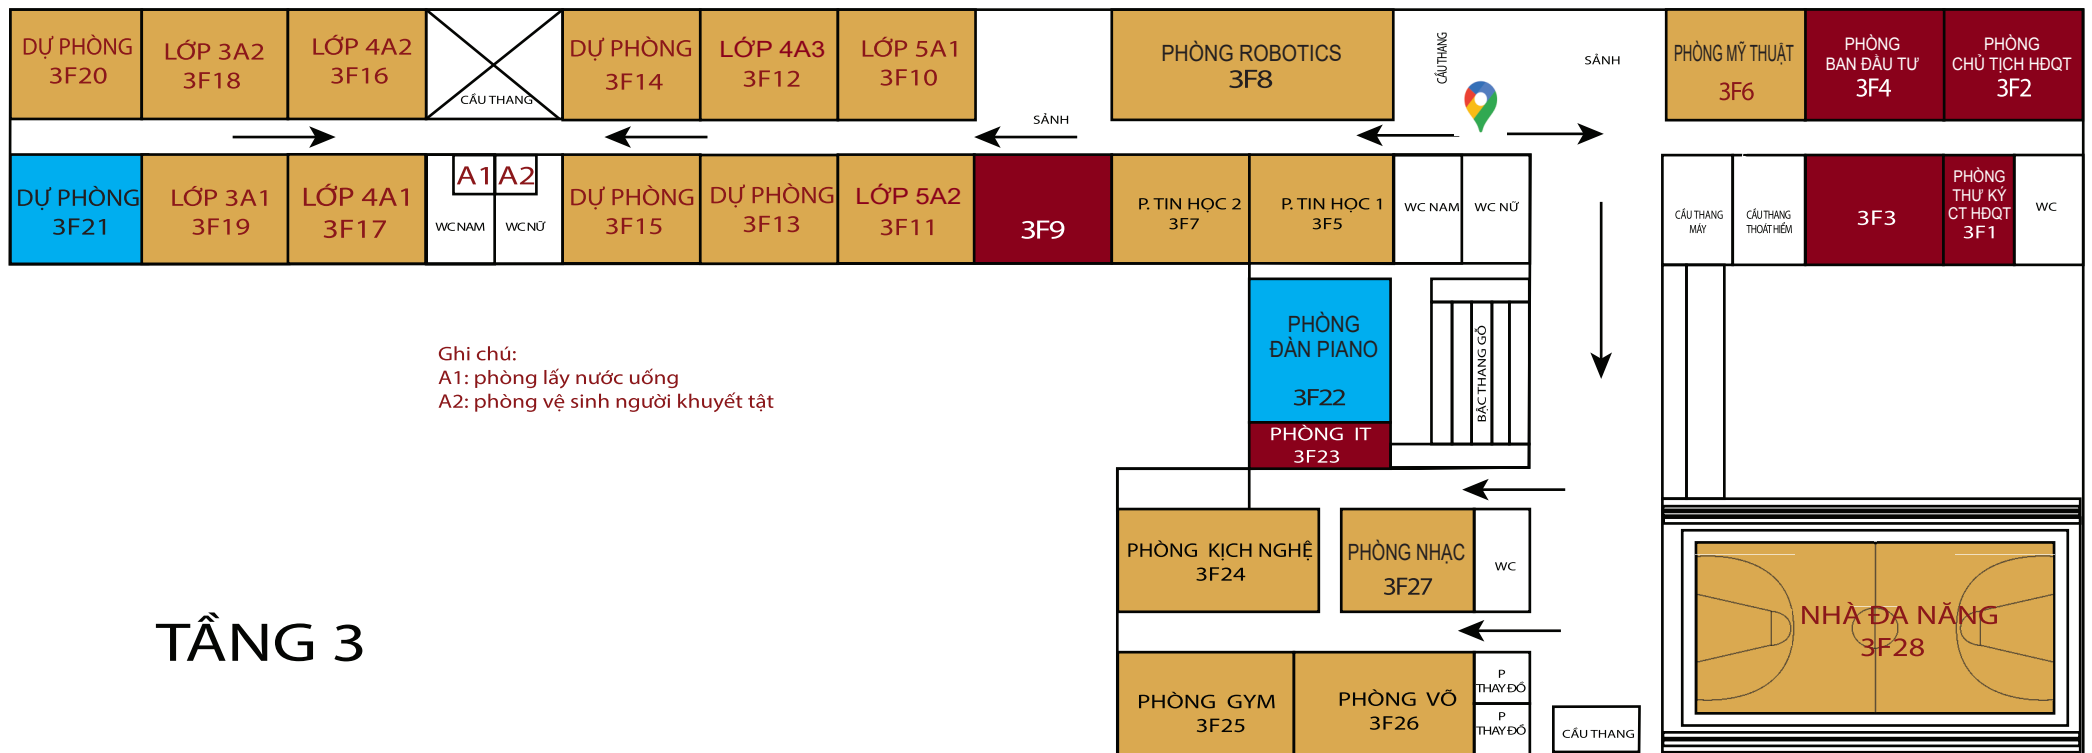


VỊ TRÍ HIỆN TẠI CỦA BẠN







VỊ TRÍ HIỆN TẠI CỦA BẠN

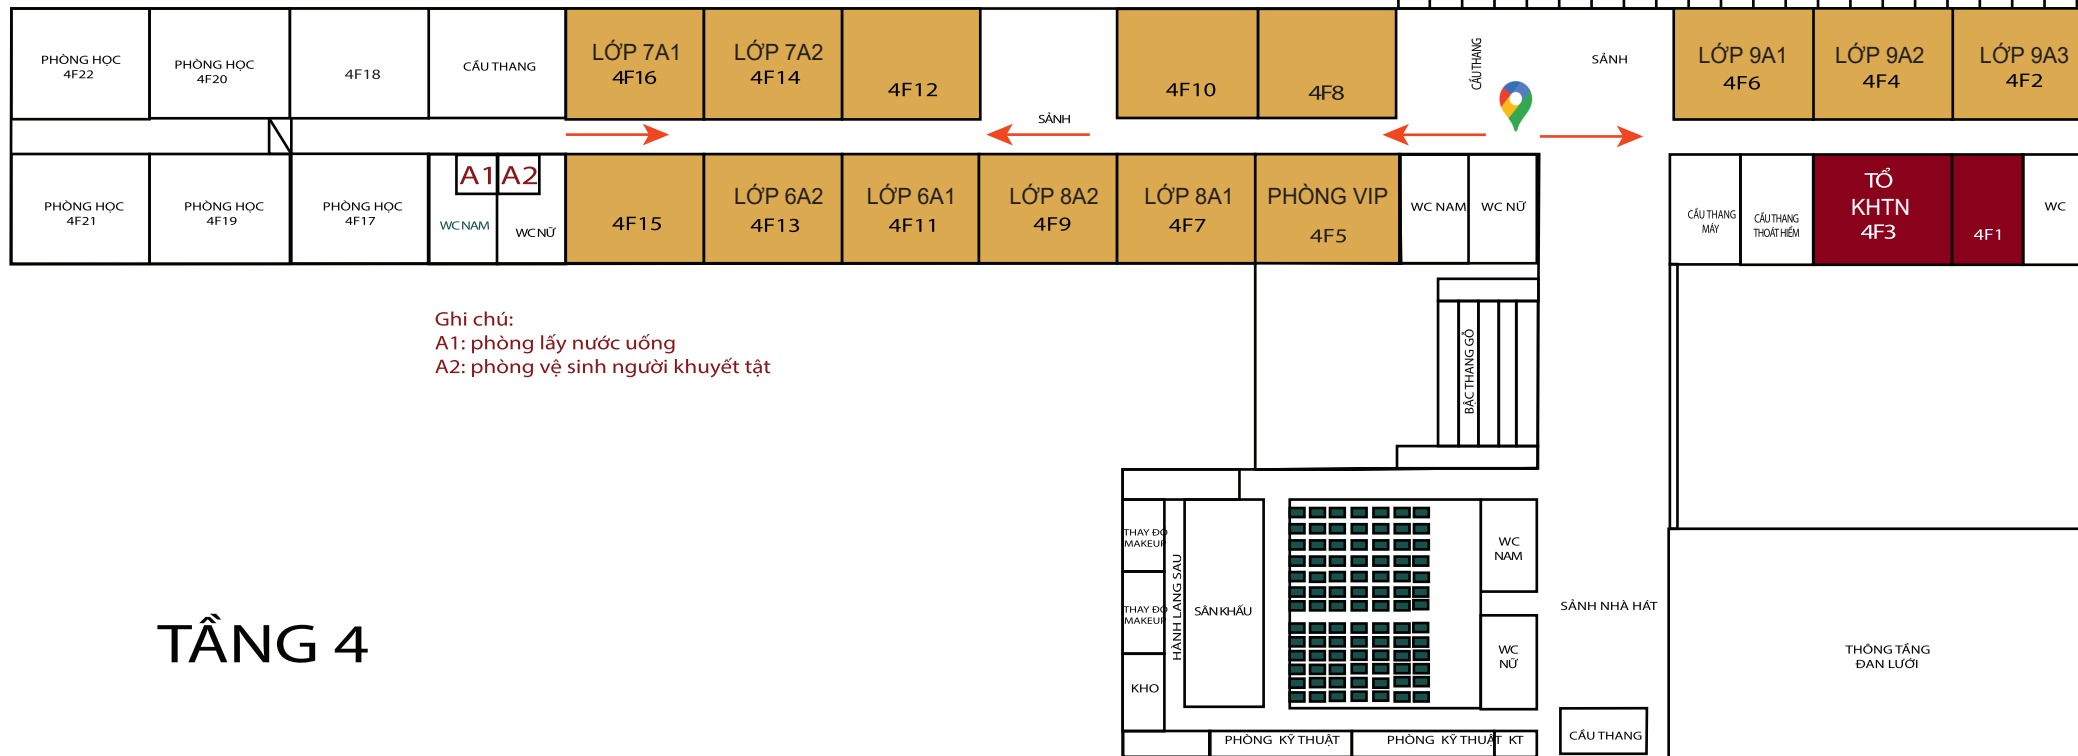


TẦNG 4


VỊ TRÍ HIỆN TẠI CỦA BẠN

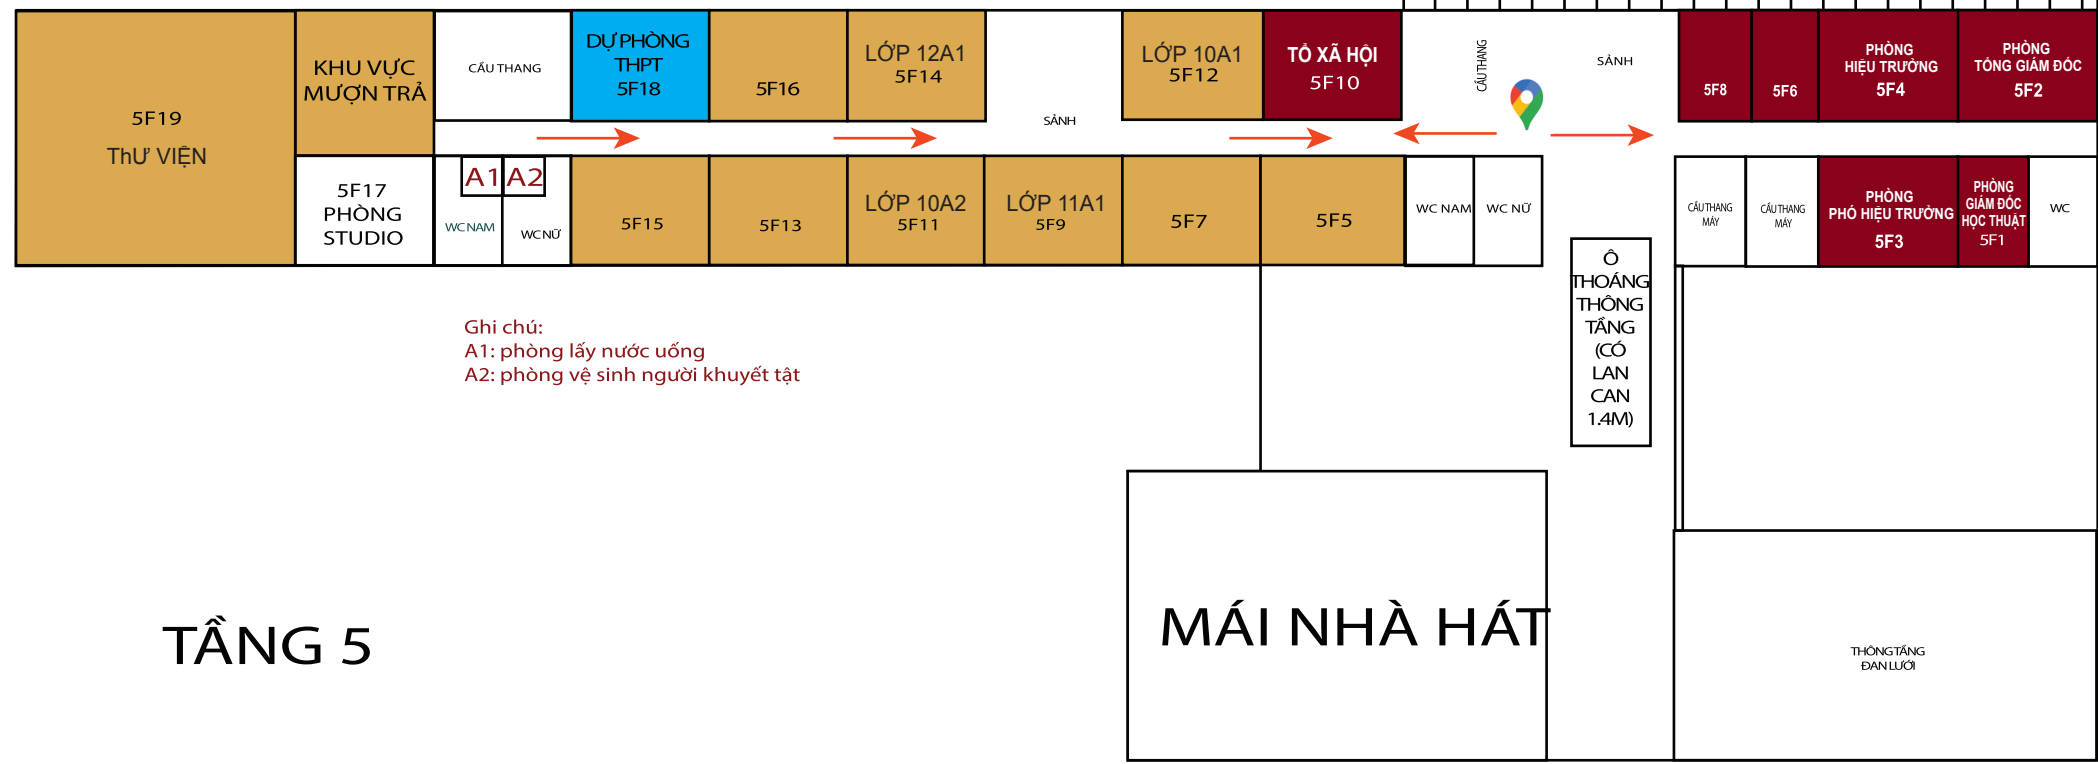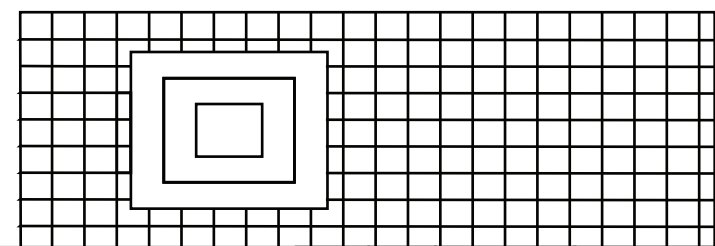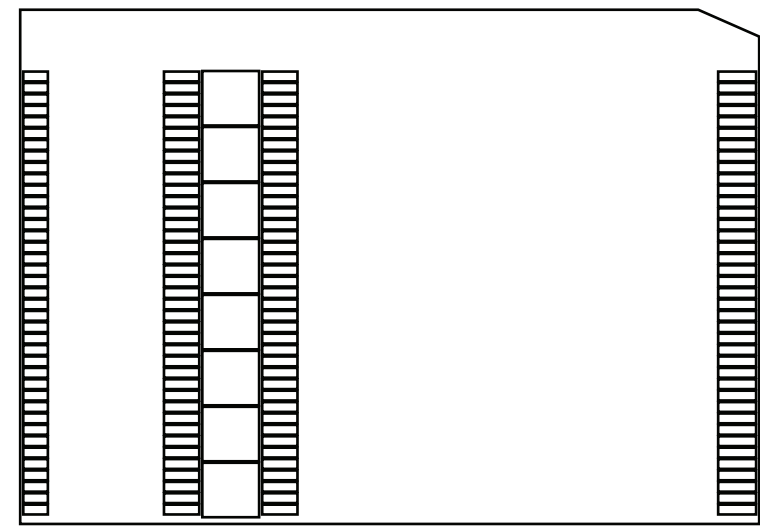

TẦNG 5

VỊ TRÍ HIỆN TẠI CỦA BẠN

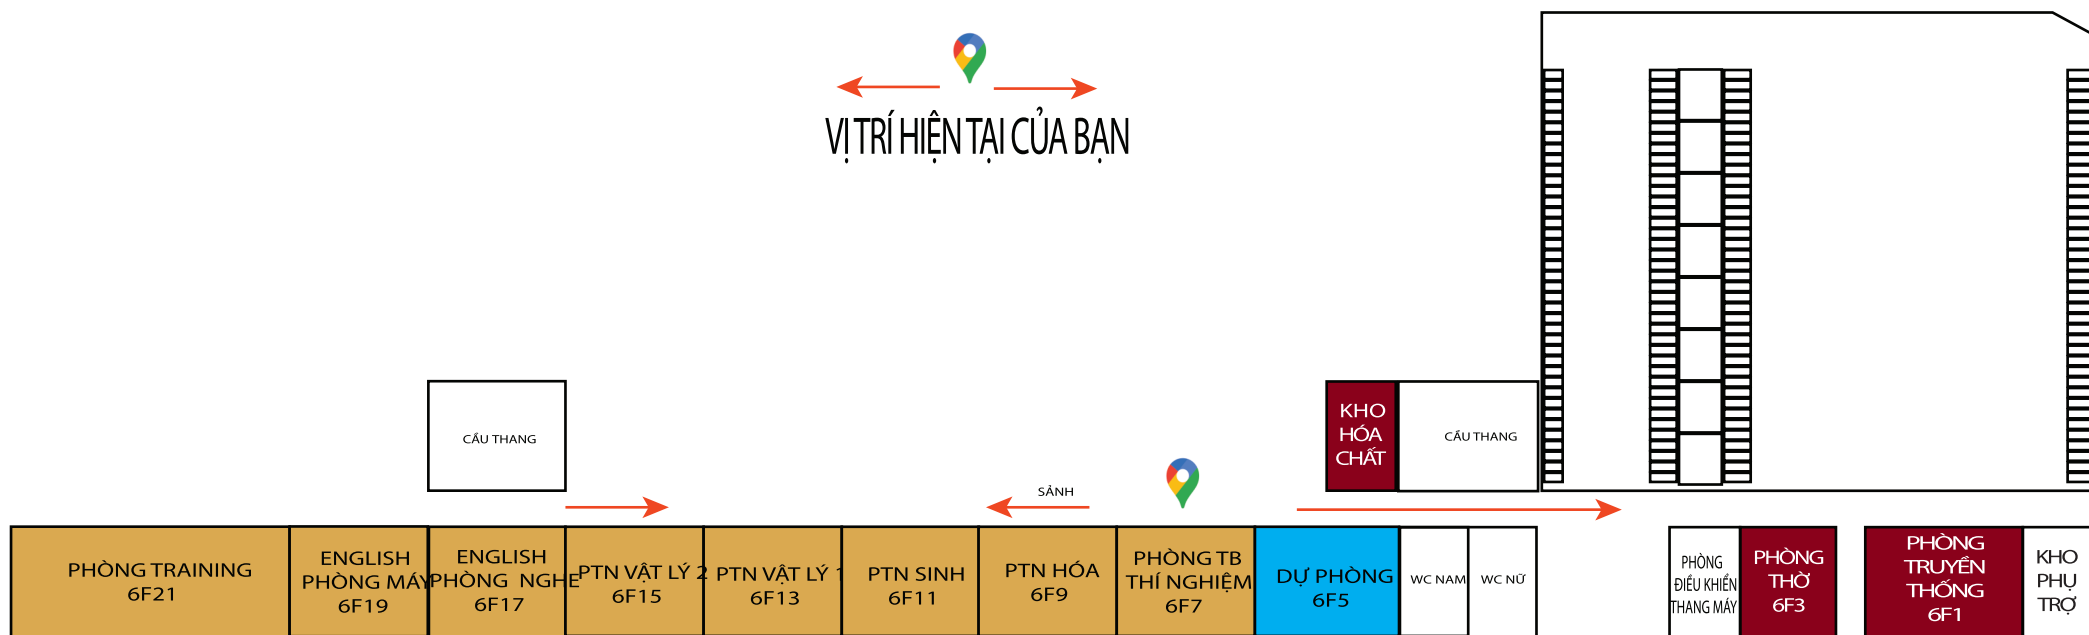

TẦNG 6

MÁI NHÀ HÁT